


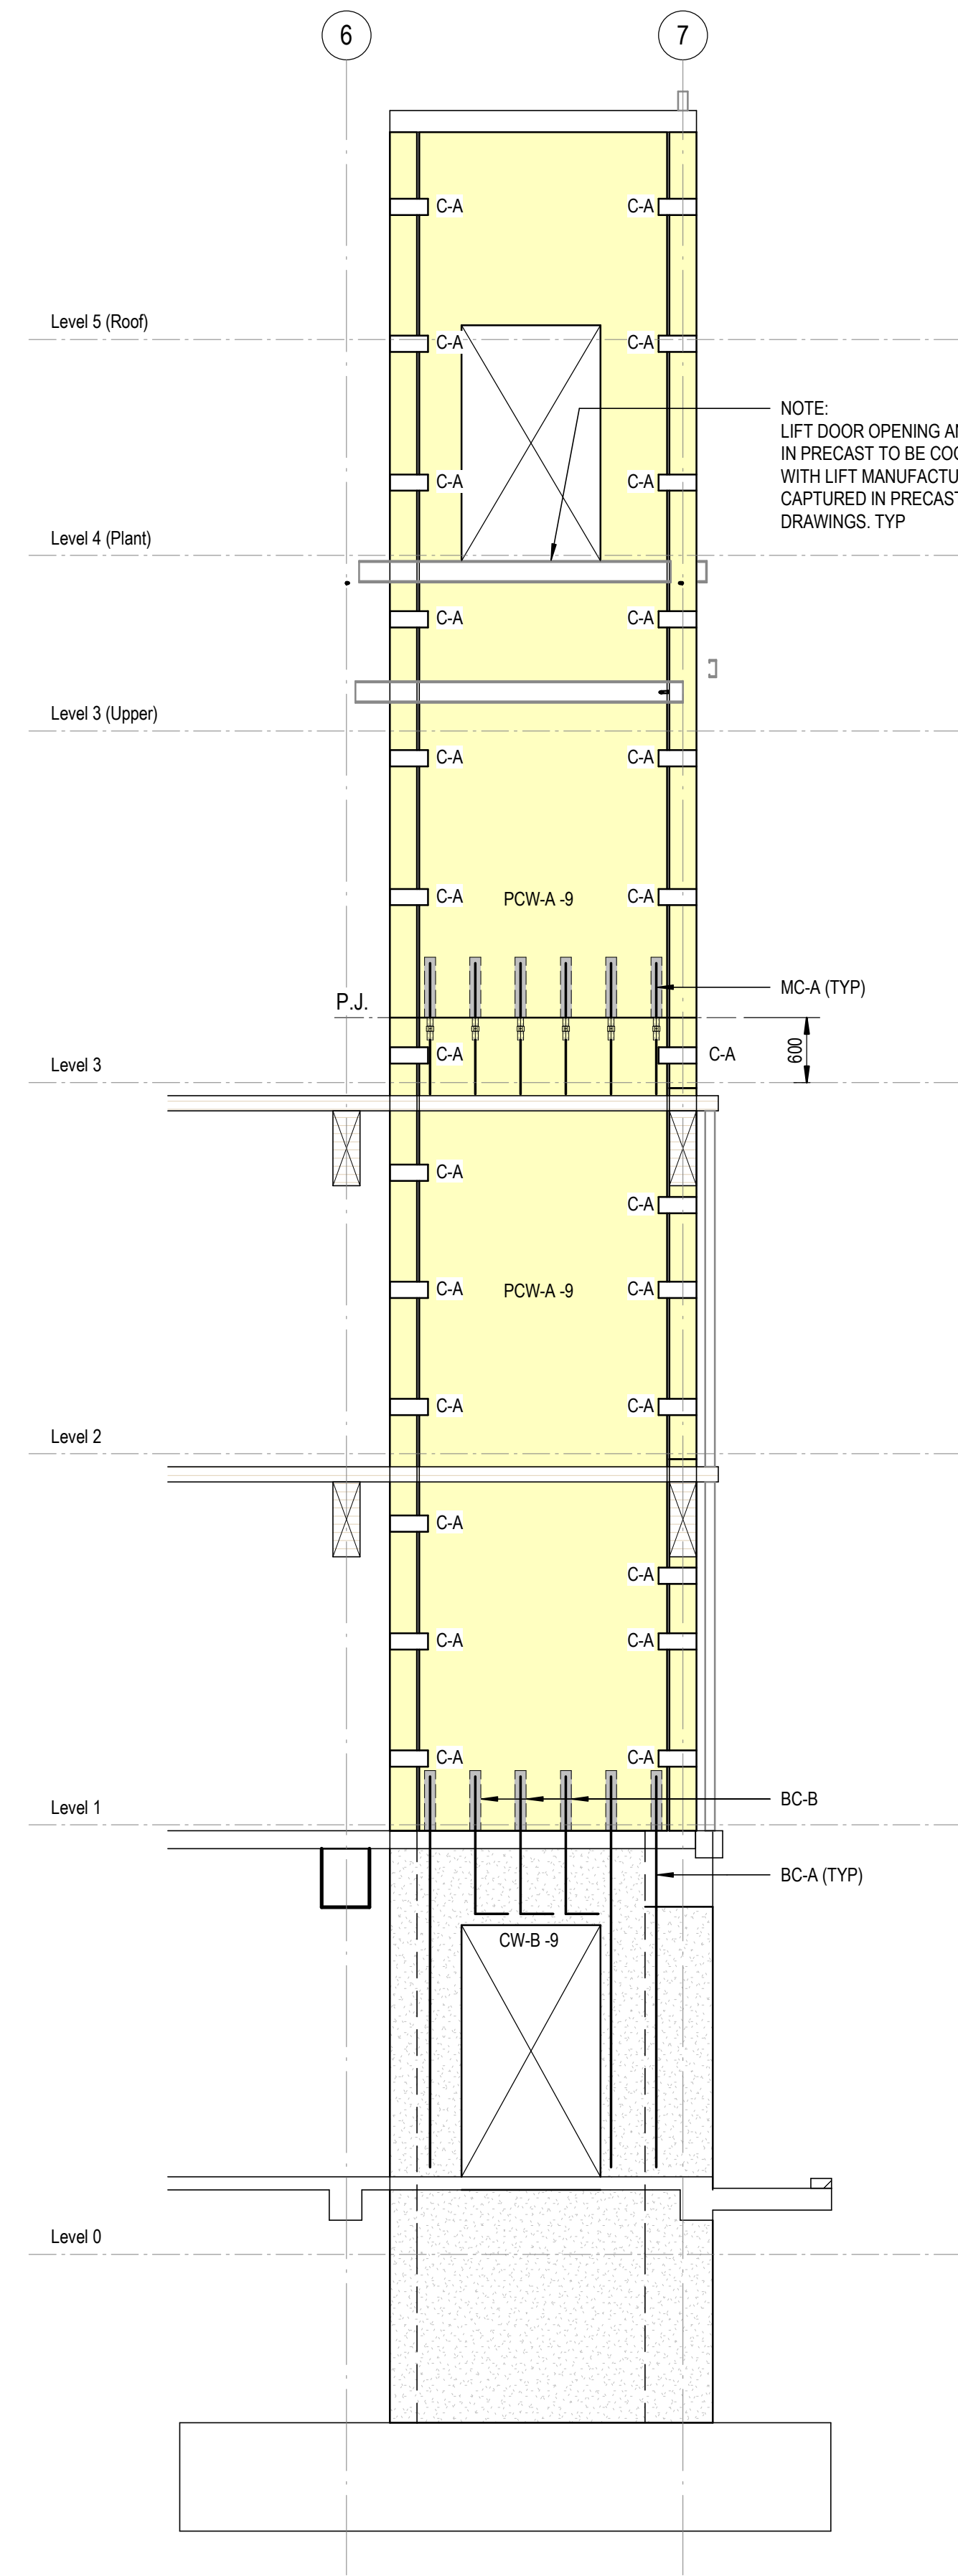

WALL 9 ELEVATION

SCALE 1:50

WALL NOTES

- ALL REINFORCEMENT SHOWN ON ELEVATIONS IS TO BE EACH FACE U.N.O.
- NF DENOTES NEAR FACE REINFORCEMENT.
- FF DENOTES FAR FACE REINFORCEMENT.
- REFER DRG. S030 FOR ADDITIONAL REINFORCEMENT AT WALL INTERSECTIONS, PENETRATIONS AND ENDS.
- THESE DRAWINGS ARE TO BE READ IN CONJUNCTION WITH STAIR DRAWINGS.
- THESE DRAWINGS ARE TO BE READ IN CONJUNCTION WITH SERVICE DRAWINGS, THE CONTRACTOR IS TO CONTACT THE STRUCTURAL ENGINEER SHOULD ANY DISCREPANCIES OCCUR.
- FOR WALLS THAT HAVE NOT BEEN ELEVATED REFER WALL SCHEDULE ON GENERAL ARRANGEMENT PLANS FOR REINFORCEMENT.

WALL SCHEDULE				
MARK	VERT REINF.	HORIZ REINF.	DESCRIPTION	REMARKS
CW-B	N16-200 E.F.	N16-200 E.F.	250 THICK CONCRETE	
CW-C	N16-200 E.F.	N16-200 E.F.	625 THICK CONCRETE	
PCW-A	REFER	DETAILS	250 THICK PRECAST	
PCW-B	REFER	DETAILS	250 THICK PRECAST	
RW1			200 SERIES BLOCKWORK	

TILT PANEL LEGEND

- C-x INDICATES CLIP LOCATION AND TYPE
- PJ INDICATES PANEL JOINT
- BC-x INDICATES BOTTOM CONNECTION. REFER TYPICAL DETAILS.
- MC-x INDICATES MID CONNECTION. REFER TYPICAL DETAILS.

BLIGH TANNER BRISBANE SYDNEY blightanner@blightanner.com.au blightanner.com.au	REV	DATE	DESCRIPTION	DRAWN	DESIGN	APPROVED	CLIENT 	ARCHITECT m3architecture	STATUS CONSTRUCTION ISSUE		DRAWN BY	M.COHEN	PROJECT MOUNT ALVERNIA COLLEGE - LIBRARY AND ASSOCIATED WORKS 82 CREMORNE ROAD, KEDRON QLD 4031									
	DESIGN BY	D.McCARRON																				
	CHECKED BY	T.MARCOT																				
														DRAWING TITLE WALL ELEVATIONS - SHEET 3								
															PRINTING REQUIREMENTS		JOB NO 2024.0097		DRAWING NUMBER S042		REVISION A	
															PRINT THIS DRAWING IN COLOUR							